



Согласовано			
Взам. инв. №			
Подп. и дата			
Инв. №подл.			


Подключение головного контроллера LED-IPСп

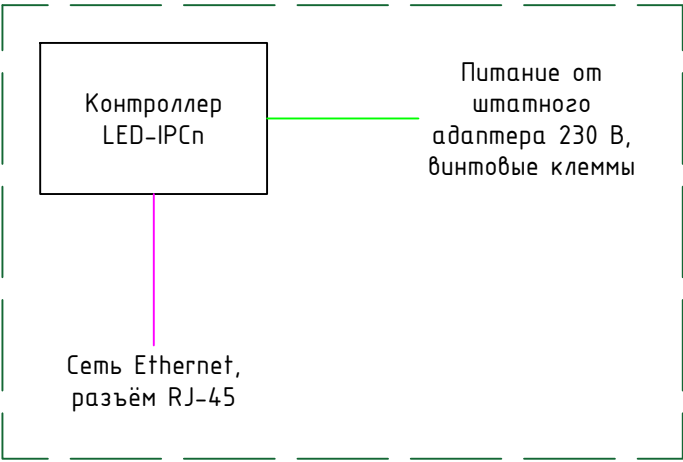


Подключение конвертера U-Box 2, типовое

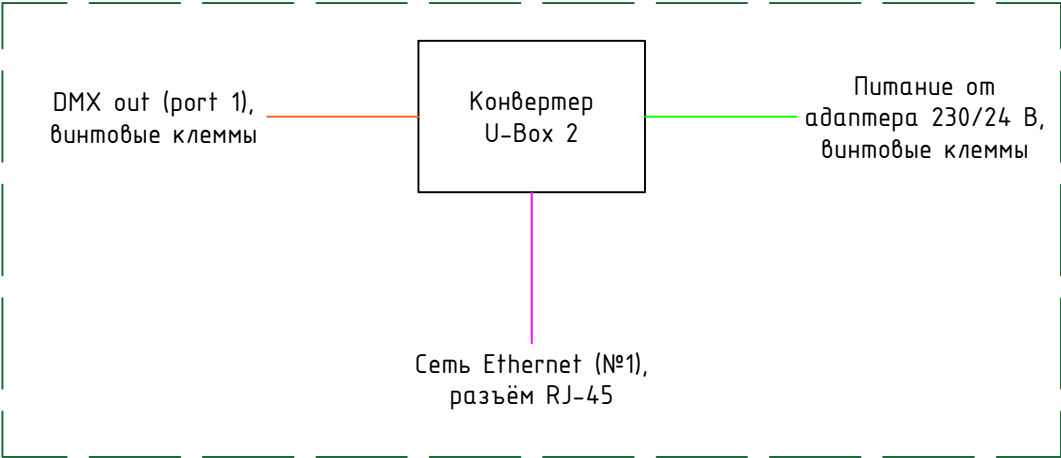


Подключение конвертера DMX-DIM, типовое

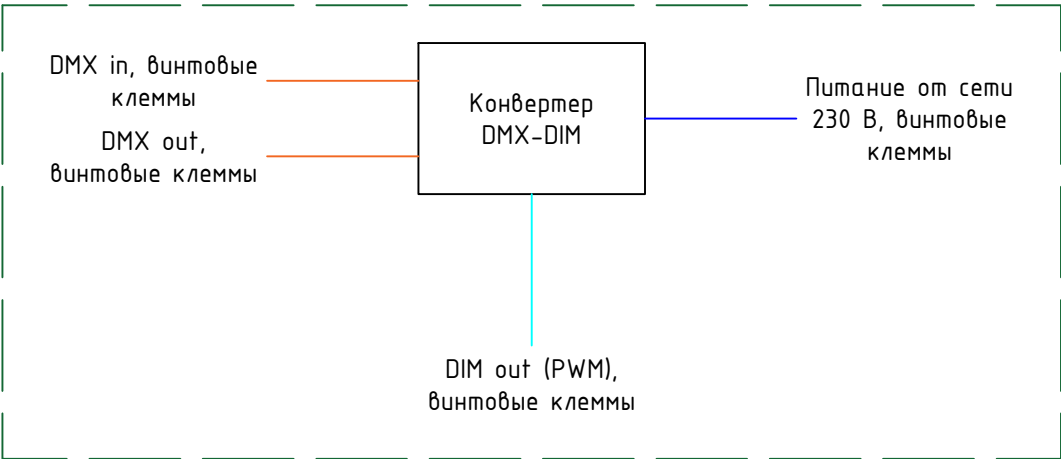


Подключение релейного DMX модуля, типовое

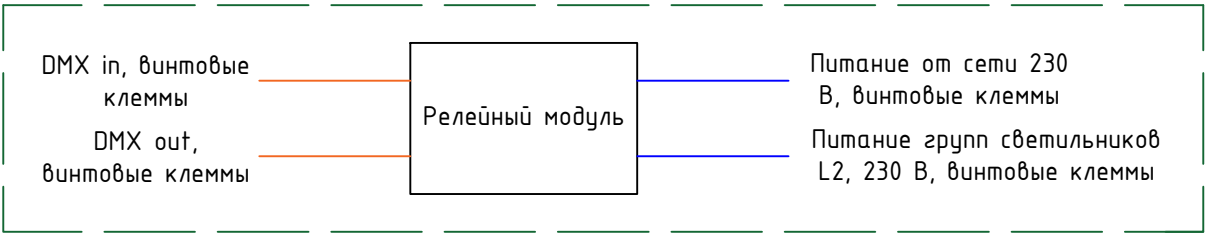

Подключение питания и управления к 1 светильнику (тип L1.X), типовое

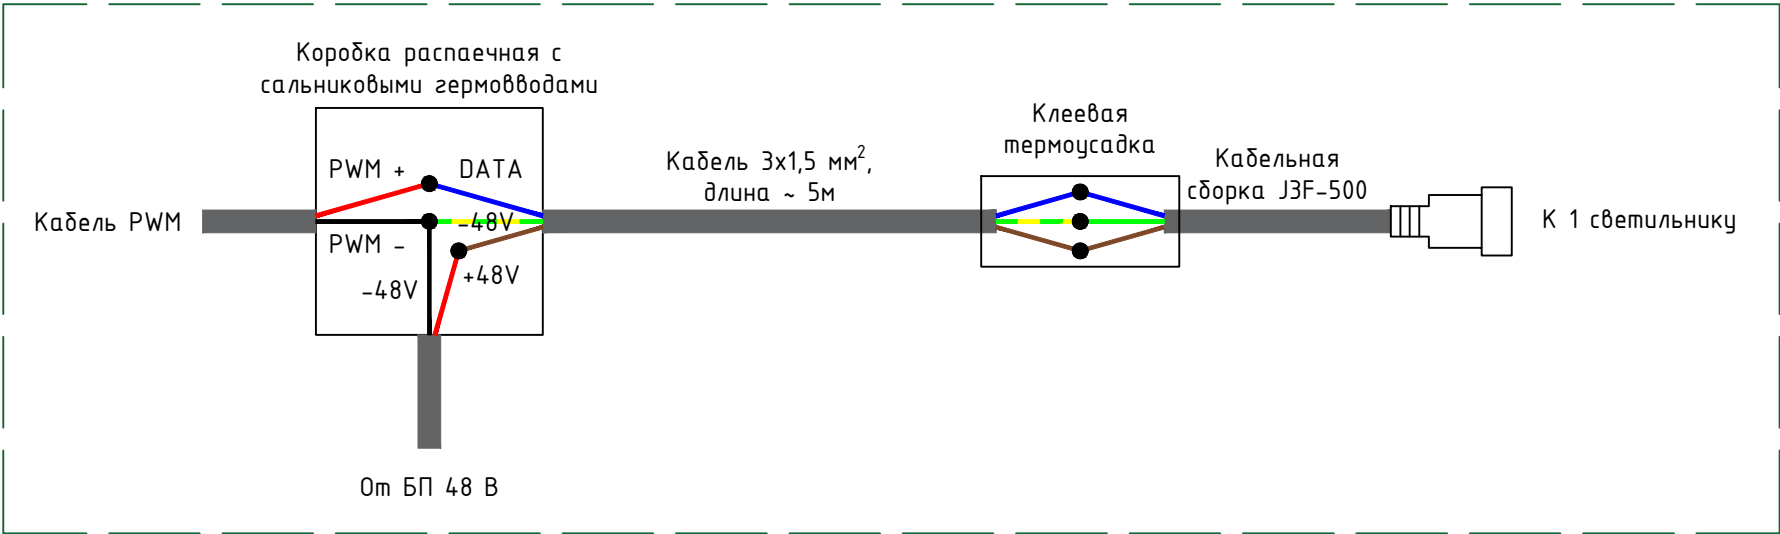

Подключение питания "в разрыв" линии светильников (тип L1.X), типовое

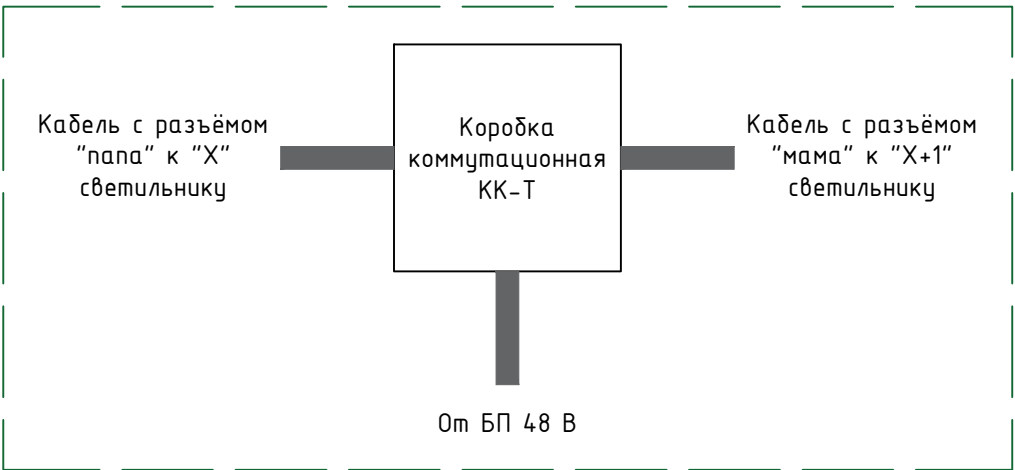

						ПСИ-158-ОБ-ИОС1.5			
						Строительство многопрофильной клиники государственного бюджетного учреждения здравоохранения Московской области «Балашихинская областная больница» по адресу: Московская область, г.о. Балашиха. Корректировка			
1	-	Нов.	44-26		03.26	Раздел 5. Подр. 1. Сист. эл-снабжения. Часть 5.	Стадия	Лист	Листов
Изм.	Колуч	Лист	№док	Подп.	Дата		П	57	1
Разраб.	Лузин				02.26				
Проверил	Ершов				02.26				
						Архитектурное освещение фасадов	 ООО "К-7"		
Н. контр.	Ишбулатова				02.26				
ГИП	Лузин				02.26				